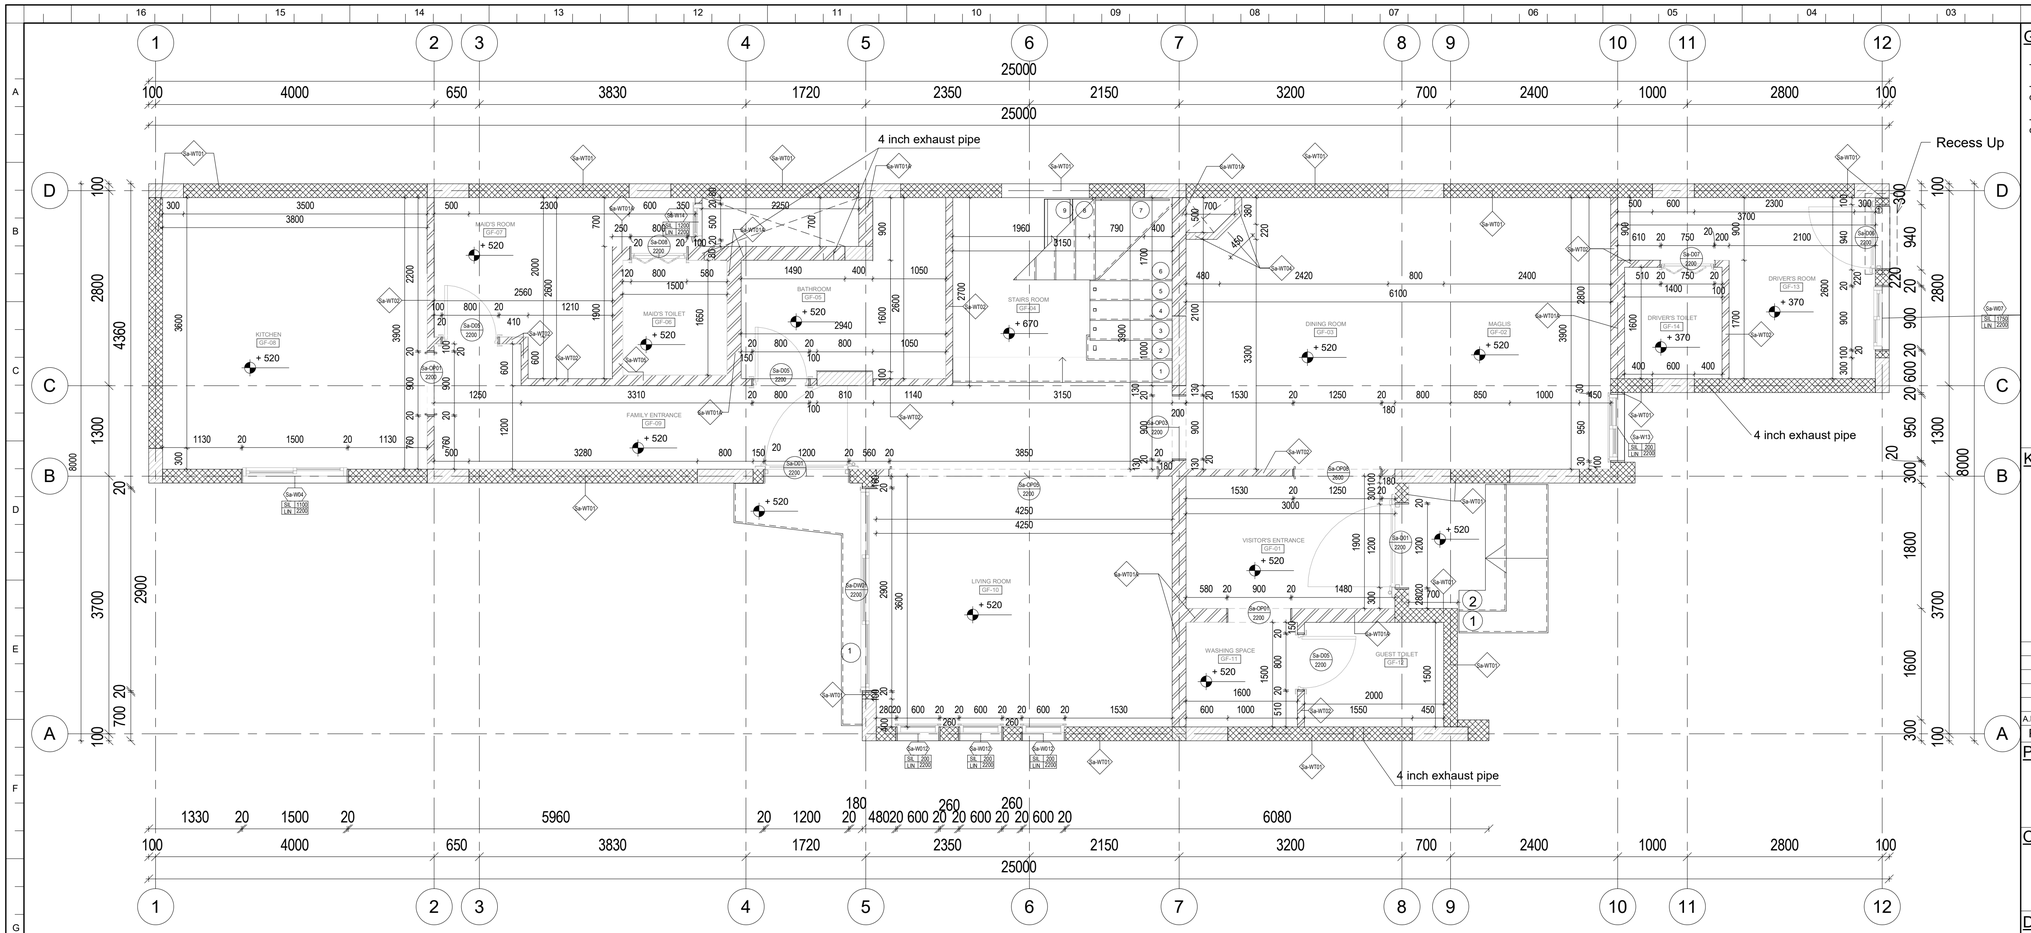

1 BLOCKWORK GF PLAN
1 : 50

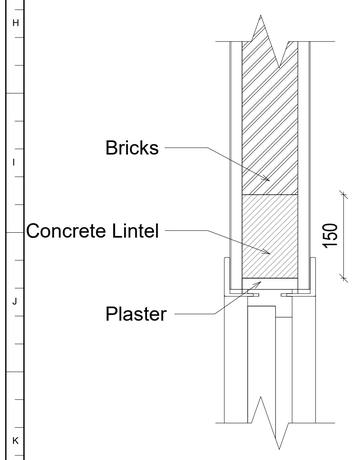

2 Typical Door opening section
1 : 5

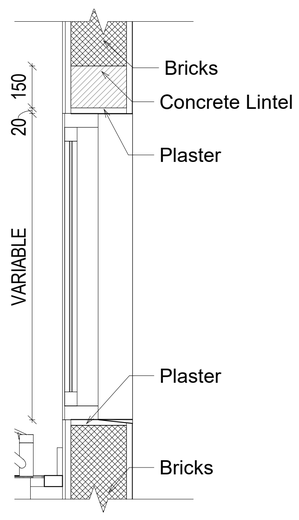

3 Typical Window opening Section
1 : 10

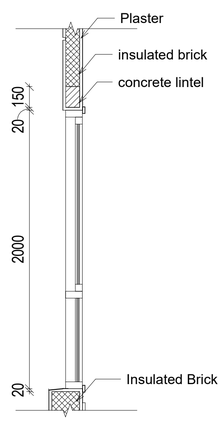

4 Typical Recess Section
1 : 20

Window TYPE C				
Type	Width	Head Height	Sill Height	Description
Sa-W03	1200	2200	200	
Sa-W04	1500	2200	1100	Sliding
Sa-W05	1500	2200	200	
Sa-W06	500	2200	200	hinged
Sa-W07	900	2200	1750	Sliding
Sa-W08	900	2450	500	fixed
Sa-w11	600	2200	200	Corner window
Sa-W012	600	2200	200	hinged
Sa-W13	950	2200	200	
Sa-W14	500	2200	1200	hinged

Wall Types			
Code	Type	Width	Description
Sa_WT01	Brick wall	200	insulated brick
Sa_WT01A	Brick wall	200	_
Sa_WT02	Brick wall	100	_
Sa_WT03	Brick wall	200	solid brick
Sa_WT04	Reinforced Concrete	100	fence wall
Sa_WT05	Brick wall	150	_
Sa_WT06	Brick wall	300	insulated brick

Door Schedule			
Type	Width	Height	Description
Sa-D01	1200	2200	Steel Door Painted
SA-D02	1200	2200	Steel Door Painted
Sa-D03	2800	2300	Garage door system BGR/SK 350
Sa-D04	900	2200	Wooden Door Composite WPC
Sa-D05	800	2200	Wooden Door Composite WPC
Sa-D06	900	2200	Steel Door Painted
Sa-D06	900	2200	Steel Door Painted
Sa-D07	750	2200	FOOLDED
Sa-D08	800	2200	FOOLDED
Sa-D09	450	1030	
Sa-DW01	2900	2200	DOOR WINDOW
Sa-DW03	1200	2000	DOOR WINDOW
Sa-DW04	3750	2000	DOOR WINDOW
Sa-OP01	900	2200	
Sa-OP03	900	2200	
Sa-OP05	3850	2200	
Sa-OP08	1250	2600	

General Notes :

- All dimension in millimeter
- Do not scale dimensions from drawings. Use given dimensions or request clarification if necessary
- Refer to specific drawings and sections for detailed construction requirements

Key Plan

Wall Hatches

Insulated Brick Wall

Brick Wall

Wall Tag — Wall Code

Window Tag — Window Code, SIL, LIN, Sill Height, Lintel Height

Door Tag — Door Code, Lintel height

Prepare	Check	Revision	Issued For	Date	REV
A.H	E.B	E.B			

Project

المشروع

مشروع سهيل جاردن
ضاحيه السدن
جده - منطقة ٧

Owner

المالك

الشركة الوطنية للإسكان
National Housing Company
NHC

Developer

المطور

مكيون
مطورون عمرانيون

Consultant

الاستشارى

المحترف
مكتب المحترف للاستشارات الهندسية

Construction Supervision Consultant

مكتب الدكتور
نبيل محمد علي عباس
استشارات هندسية

Contractor Consultant

الاستشارى المصمم

MEDAD ENGINEERING CONSULTANT
SEQUENCE ENGINEERING SERVICES

Drawing Title

TYPE C GROUND BLOCKWORK and TYPICAL OPENINGS SECTIONS

Proj. NO	Size	Date
2315	A1	03/02/2025

Scale	Drawing NO.
As indicated	SJ-SD-C-AR-BW-GF-100-R1

ALL IDEAS , DESIGNS , ARRANGEMENTS & PLANS INDICATED IN THIS DRAWING ARE OWNED BY & PROPERTY OF MEDAD CONSULTANT ENGINEERS & WERE DEVELOPED FOR USE ON & IN CONNECTION WITH THE SPECIFIED PROJECT. NONE OF SUCH IDEAS , DESIGNS , ARRANGEMENTS OR PLANS SHALL BE DISCLOSED TO ANY PERSON , FIRM OR CORPORATION FOR ANY PURPOSE WHAT SO EVER WITHOUT THE WRITTEN PERMISSION FROM MOHTARIF CONSULTANT ENGINEERS.